

PULSING CHAK ON


STORIES, SPACE, CONNECTION

S-MAFM6X

01/02

BACKGROUND


SITE SITUATION

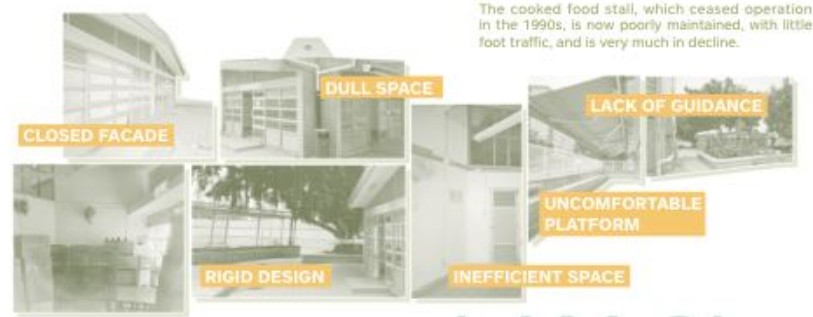

RESIDENTS' NEEDS



MASTERPLAN

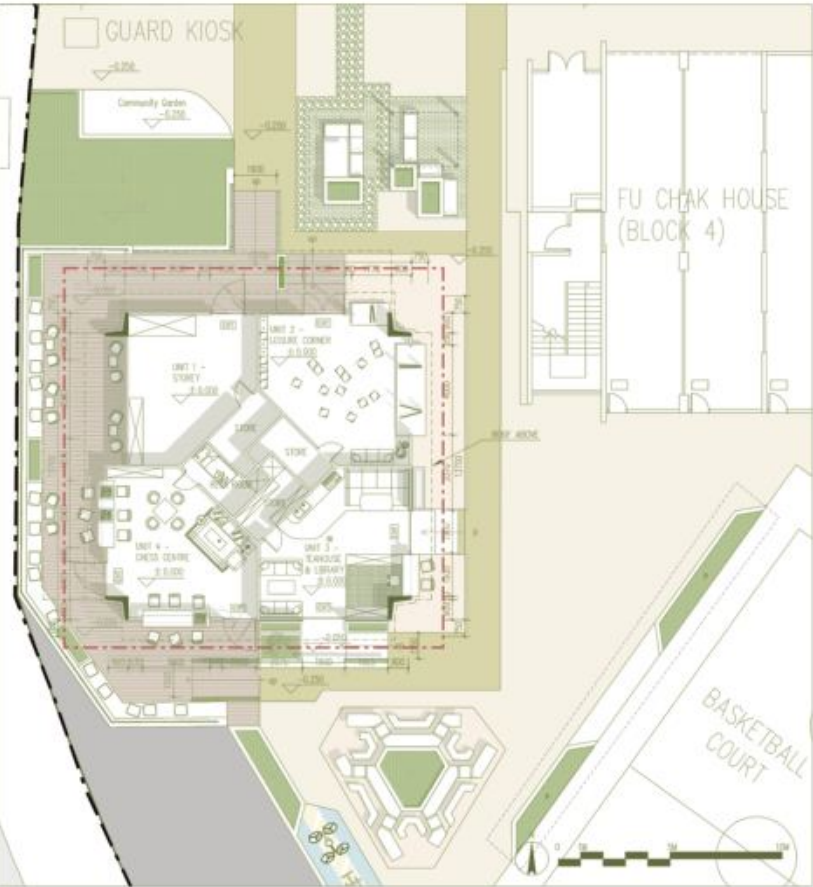

DESIGN STRATEGY

I. Functional Flexibility · Spatial Hybridity

ENHANCE SPATIAL ADAPTABILITY THROUGH SCENARIO-BASED LAYOUTS AND MULTI-FUNCTIONAL UTILIZATION.

SCENARIO DESIGN



MODULAR FURNITURE



III. Spatial Synergy · Borderless Integration

BLUR INTERIOR-EXTERIOR BOUNDARIES TO AMPLIFY SPATIAL INTERACTIVITY AND CONTINUITY, FOSTERING OPEN AND VIBRANT SHARED ENVIRONMENTS.

OUTDOOR REVITALIZATION



CANOPY SYSTEM



IV. Universal Inclusion · All-Age Community

CREATE BARRIER-FREE, EMPATHETIC SPACES CATERING TO DIVERSE GENERATIONAL NEEDS.

RESTING FACILITIES



II. Community Curation · Identity Reimagined

STRENGTHEN NEIGHBORHOOD IDENTITY AND COLLECTIVE PRIDE THROUGH ENHANCED ENTRY SYMBOLISM AND PUBLIC IMAGERY.

GATEWAY IDENTITY



LAYERED GREENERY



INTERACTIVE INTERFACES



V. Dynamic Facilities · Shared Vitality

ENHANCE SPATIAL ADAPTABILITY THROUGH SCENARIO-BASED LAYOUTS AND MULTI-FUNCTIONAL UTILIZATION.

WELLNESS INSTALLATIONS



PULSING CHAK ON

STORIES, SPACE, CONNECTION

S-MAFM6X

02/02

BACKGROUND

SITE SITUATION

LOW ACTIVITY

EMPTY PLAZA

MESSY PAVING

OLD FACADE

VAGUE SIGNAGE

LACK OF USAGE

DIS-ORGANIZED

With poor accessibility and inadequate maintenance, the plaza rarely used by residents results in inconvenience.

RESIDENTS' NEEDS


ONLY ONE RAMP TO THE PLAZA!

I RATHER GO ACROSS THE PLAZA THEN WALK ON THE ROAD.

MORE ACTIVITIES
WALKABILITY
COLORS
NEW RAMP
WELL-BEING
MID-AUTUMN GALA
SHADE
DANCING
NGO
COMFORTABLE SEATS

HOPING FOR MORE EVENT HERE

MASTERPLAN

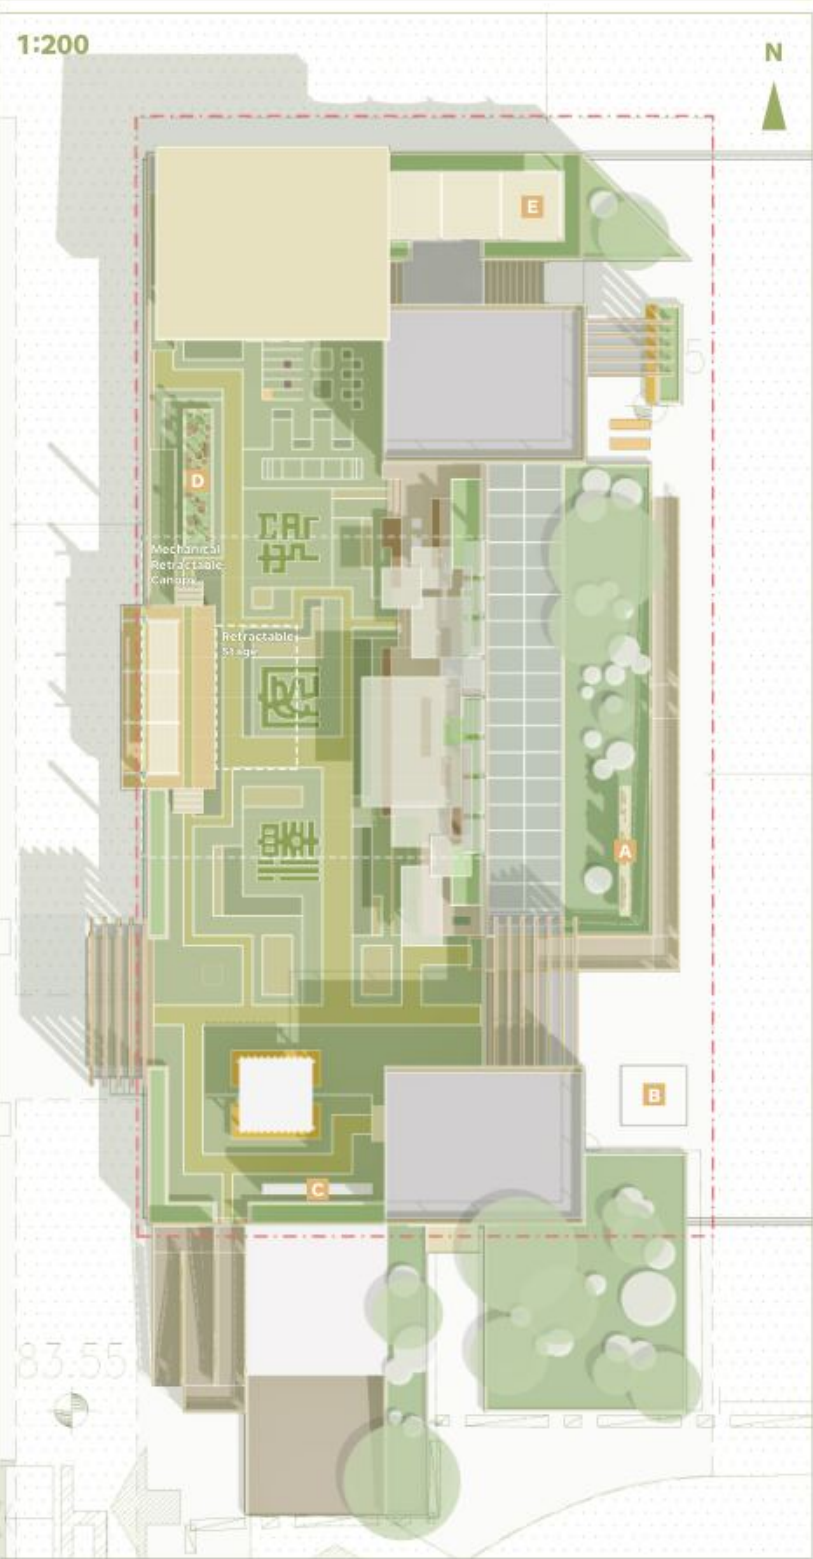

DESIGN STRATEGY

I. Narrative Landscape · Story Space

WEAVE STORYTELLING CLUES THROUGH CIRCULATION, GUIDING EMOTIONAL EXPERIENCES VIA TO CREATE SPATIAL NARRATIVES WITH MEMORABLE ANCHORS.

CIRCULATION & NODES

ACCESS & INCLUSIVITY

A Artistic Signage
A beloved symbol among residents, reimagined with a fresh appearance.

B Festive Window
Showcases sculptures or structures themed for specific seasons or festivals.

C Flip Blocks
A large interactive wall that can display co-created patterns.

D Touch Notes
An interactive installation that emits corresponding musical notes when touched.

E Wind Chimes
Wind chimes swaying with the breeze, producing clear and melodious sounds.

II. Functional Reconfiguration · Sequential Organization

REORGANIZE SPATIAL ZONES BASED ON USER NEEDS, CHOREOGRAPHING BEHAVIORS THROUGH SPATIAL SEQUENCES TO ENHANCE SITE LOGIC.

SEQUENTIAL FLOW

Create Smooth Spatial Transitions Using Narrative Logic & Define Functional Clusters To Optimize Spatial Efficiency.

ZONING STRATEGY

- Prelude: Festive Showcase**
Display Viewing
- Beginning: Restful Courtyard**
Rest Socializing
- Development: Starlight Stage**
Performance Rest
Speech Entertainment
Market Exercise
- Climax: Interactive Wonderland**
Games Entertainment
Exercise Dining
Gathering
- Conclusion: Diverse Realm**
Socializing Entertainment
Gathering
- Epilogue: Restful Station**
Rest Socializing

III. Memory Rebirth · Community Identity

FUSE LOCAL CULTURE WITH HISTORICAL MEMORIES, USING ICONIC ELEMENTS TO EVOKE EMOTIONAL RESONANCE AND FORGE RECOGNIZABLE "MEMORY LANDMARKS".

COMMUNITY STAGE

ESTATE LEGACY

GAMING AREA

STAGE OVERVIEW

EAST ENTRANCE

ABOVE STAGE

IV. Vibrant Synergy · Chromatic Living

INFUSE SPACES WITH COLOR AND DYNAMISM THROUGH MODULAR FACILITIES AND MATERIAL SYSTEMS, FOSTERING RESIDENT INTERACTION AND SHARED VITALITY.

VITALITY CANOPY

MATERIAL PALETTE

COLOR PALETTE

HEIGHT

GREY
CREAM
SAGE
WOOD
SAND
OLIVE

SHELTER

SUPPORT
SEAT
DECK
LAND

MATERIAL

WOOD PLANK
TIMBER
LIFE WHITE STEEL
LIGHT GREEN STEEL
YELLOW
HAIR
YELLOW MESSIAH
PLASTIC FLOORING

ADAPTIVE MODULES

Daily Leisure & Flexible Stage

Market, Display & Performance

Community Gathering

